

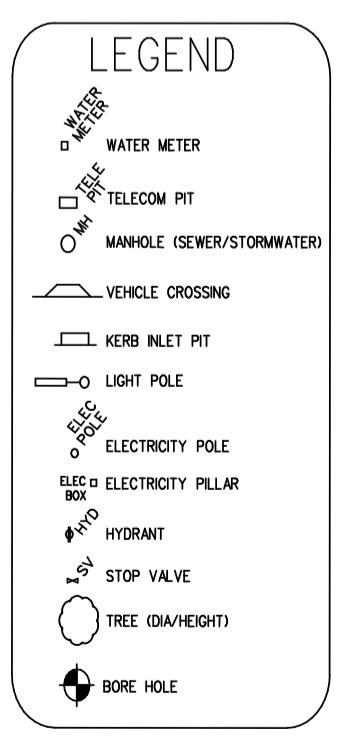


DATUM OF LEVELS: AUSTRALIAN HEIGHT DATUM  
ORIGIN OF LEVELS: PM 53389 RL 44.869  
SOURCE OF LEVELS: SCIMS

99 DENOTES PHOTO POINT

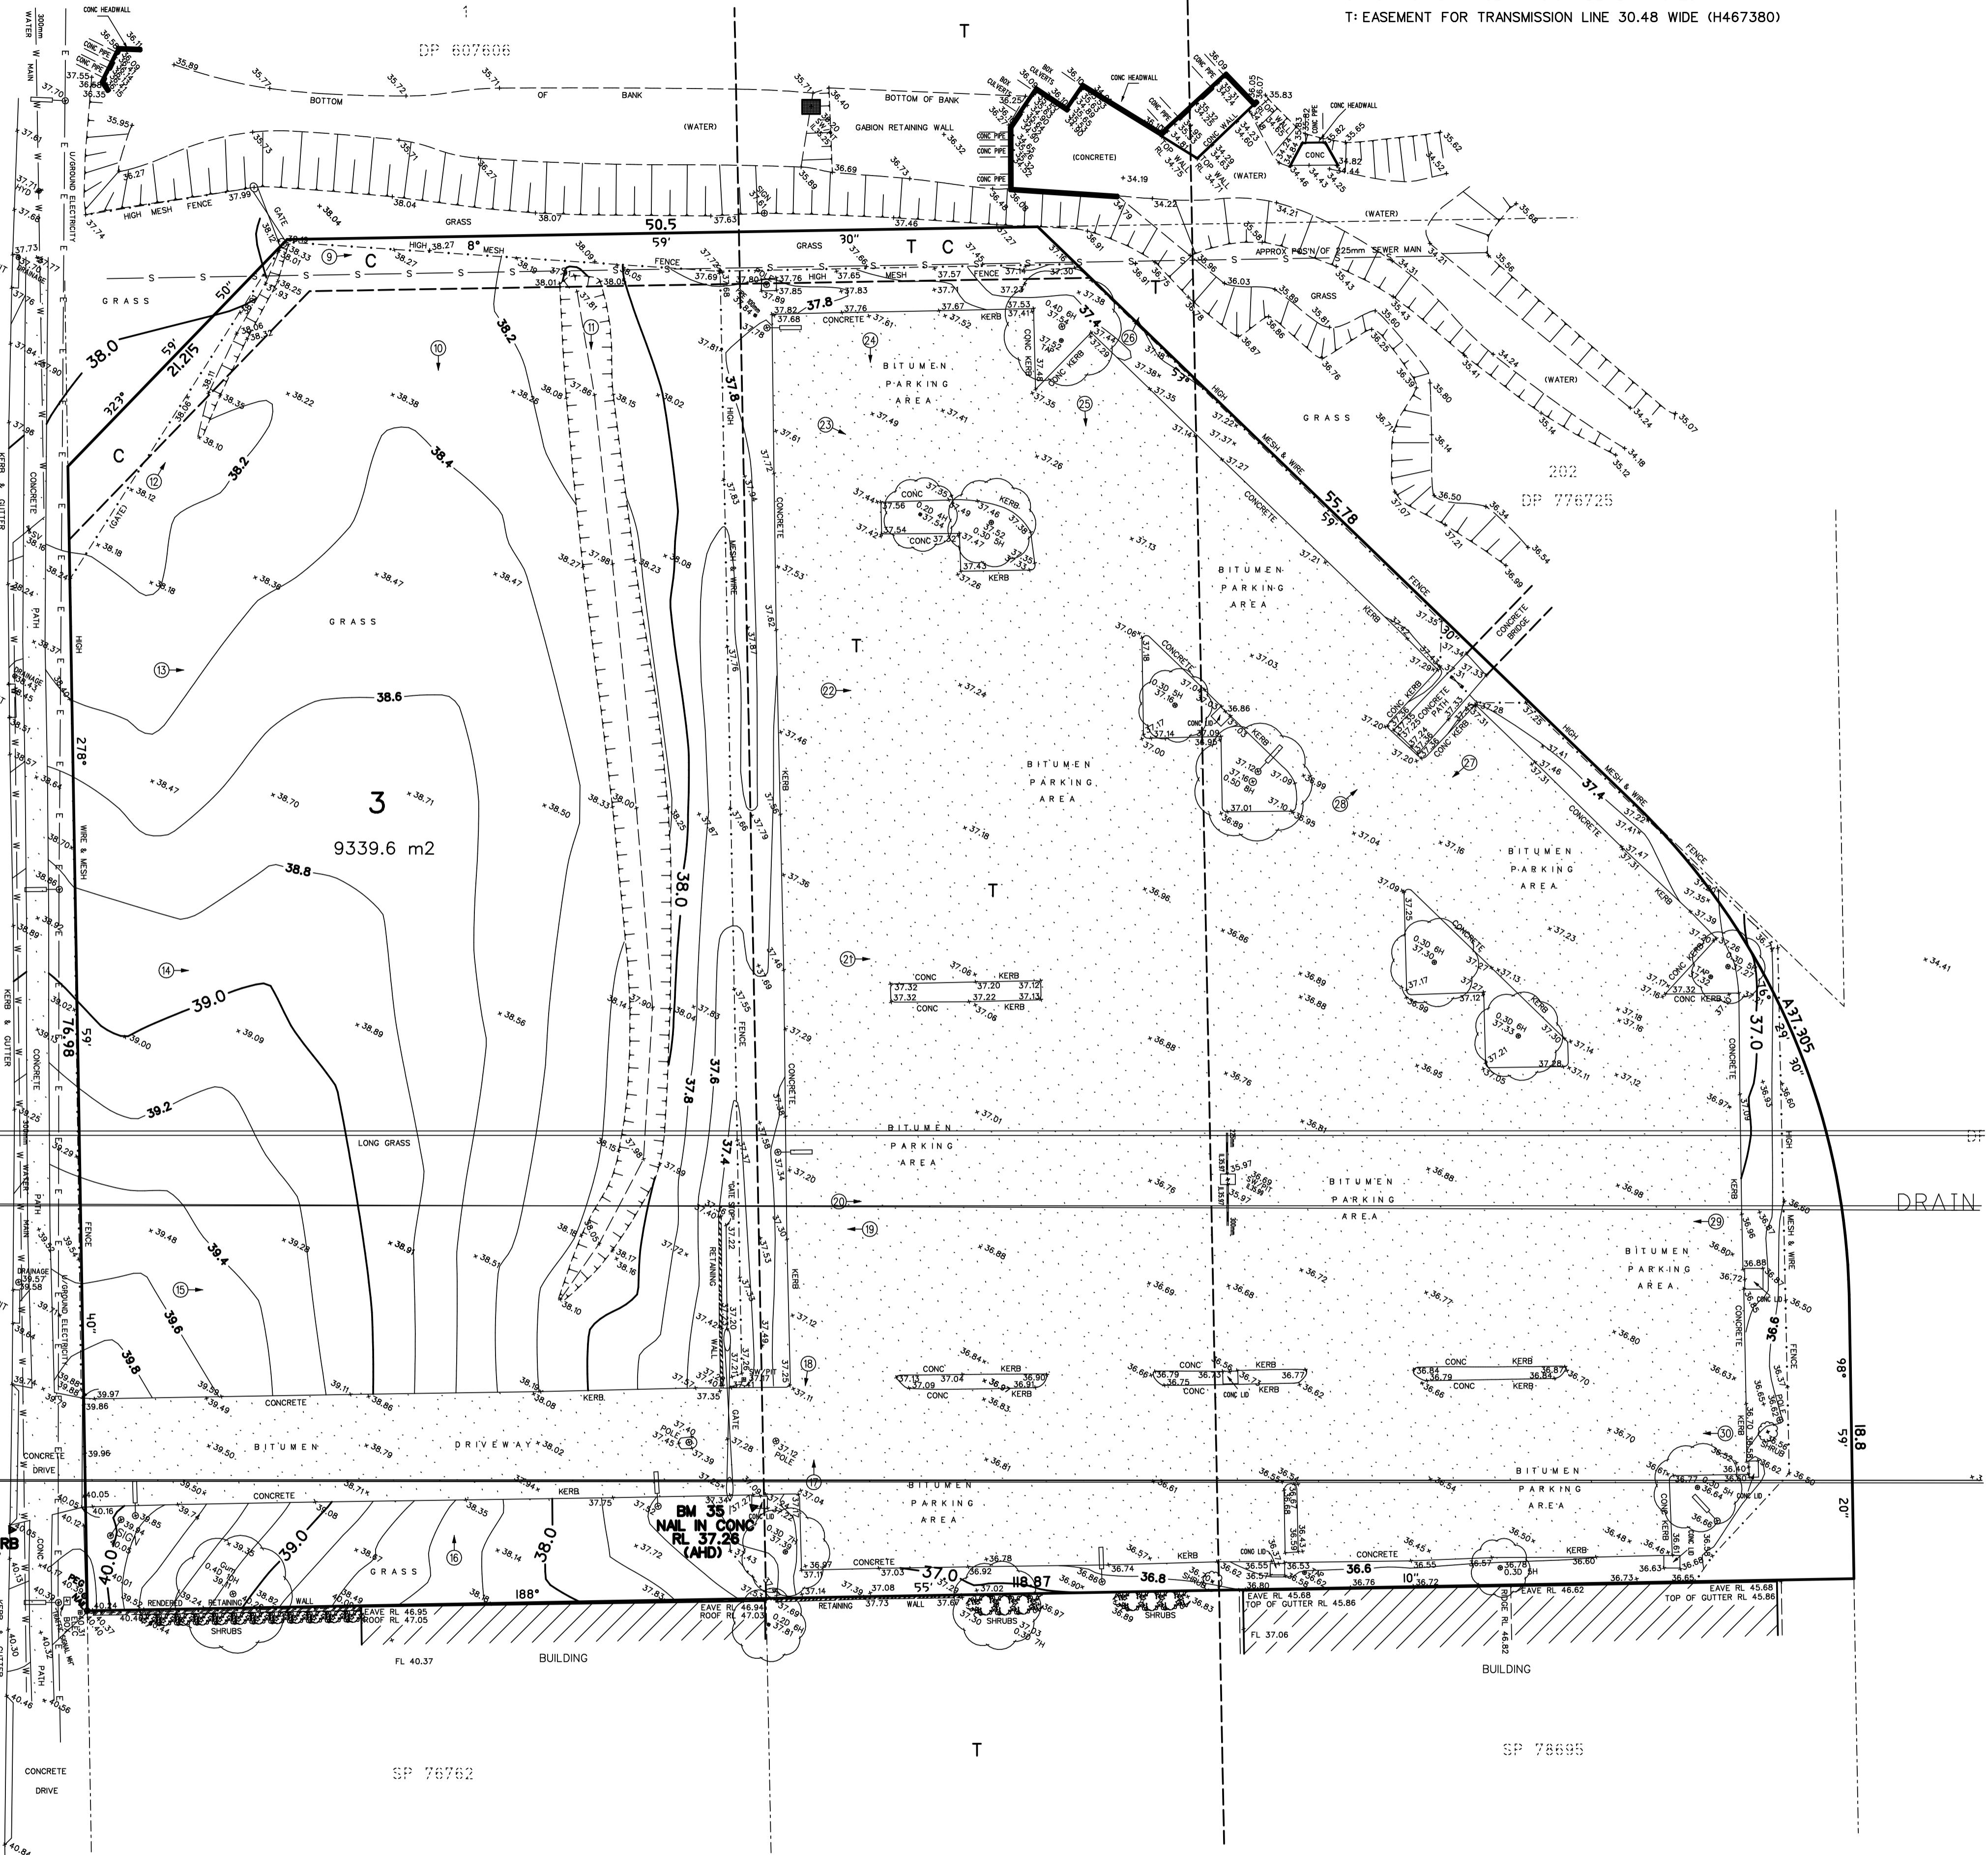

LEGEND  
KO: DENOTES KERB OUTLET  
W: DENOTES WATER CONDUIT  
SV: DENOTES STOP VALVE  
HYD: DENOTES HYDRANT

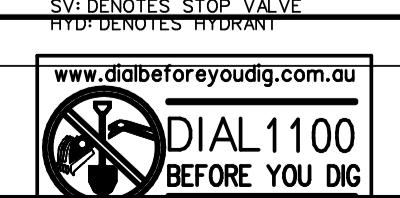

**DONOVAN**  
ASSOCIATES

INCORPORATED SURVEYORS PTY LTD ABN 84 134 616 078  
PH: 9806 3000 F: 9891 2808 www.donovanassociates.com

15 PARKES STREET PARRAMATTA NSW 2150  
CIVIL, STRUCTURAL, HYDRAULIC ENGINEERS  
REGISTERED SURVEYORS & LAND INFORMATION CONSULTANTS

NOTE: CONTOURS SHOWN HAVE BEEN INTERPOLATED FROM SPOT LEVELS TAKEN ON-SITE AND ARE A REPRESENTATION OF THE TOPOGRAPHY AT THE TIME OF SURVEY.

DIMENSIONS SHOWN BEARING A DISTANCE HAVE BEEN DETERMINED BY LAND AND PROPERTY INFORMATION PLANS ONLY. BOUNDARIES HAVE NOT BEEN ACCURATELY DETERMINED.

SERVICES SHOWN HAVE BEEN LOCATED WHERE POSSIBLE BY SURVEY. NO GUARANTEE IS MADE AS TO THEIR EXACT POSITION.

AUTHORITY SHOULD BE CONTACTED TO DETERMINE EXACT POSITION OF ANY UNDERGROUND PIPES, CABLES, ETC.

DIMENSIONS OF ANY TREES SHOWN ON THE PLAN ARE APPROXIMATE.

No. DATE NOTATION/AMENDMENT

1 30.08.2012 EXTRA DETAILS FOR DRAINAGE

DRAWN: IS DRAW 2026/129435 DATE: 09.07.2012

CHECKED: GT DGN 129435 DATUM:AHD

SCALE: 1:250